



5- While jurisdictional standards mandate a minimum of **154 parking stalls**, the Albuquerque Islamic Center recognizes that peak demand may necessitate further volume. Drawing from operational data at their current Manuel Street site, the plan provides for **up to 235 parking spaces**. This **notable surplus** guarantees that even during biennial festivals, all attendee vehicles are accommodated **entirely on-site**, effectively eliminating any parking impact on the neighboring public streets.

6- The designated parking area facilitates an efficient **internal queuing system** for school-related drop-offs and pick-ups; therefore, maintaining this **open space** is vital for fluid traffic control, independent of jurisdictional minimum requirements.

- **Calculated Requirement:** Based on the above facts a total of **154 required parking spaces**.
- **Proposed Provision:** The site plan provides **235 parking spaces**—exceeding the legal requirement by **52%**. > This surplus ensures that all student drop-off, staff parking, and congregational activities occur entirely on-site, preventing any "overflow" into the surrounding neighborhood and ensuring a safe, fluid traffic pattern even during peak transition times.

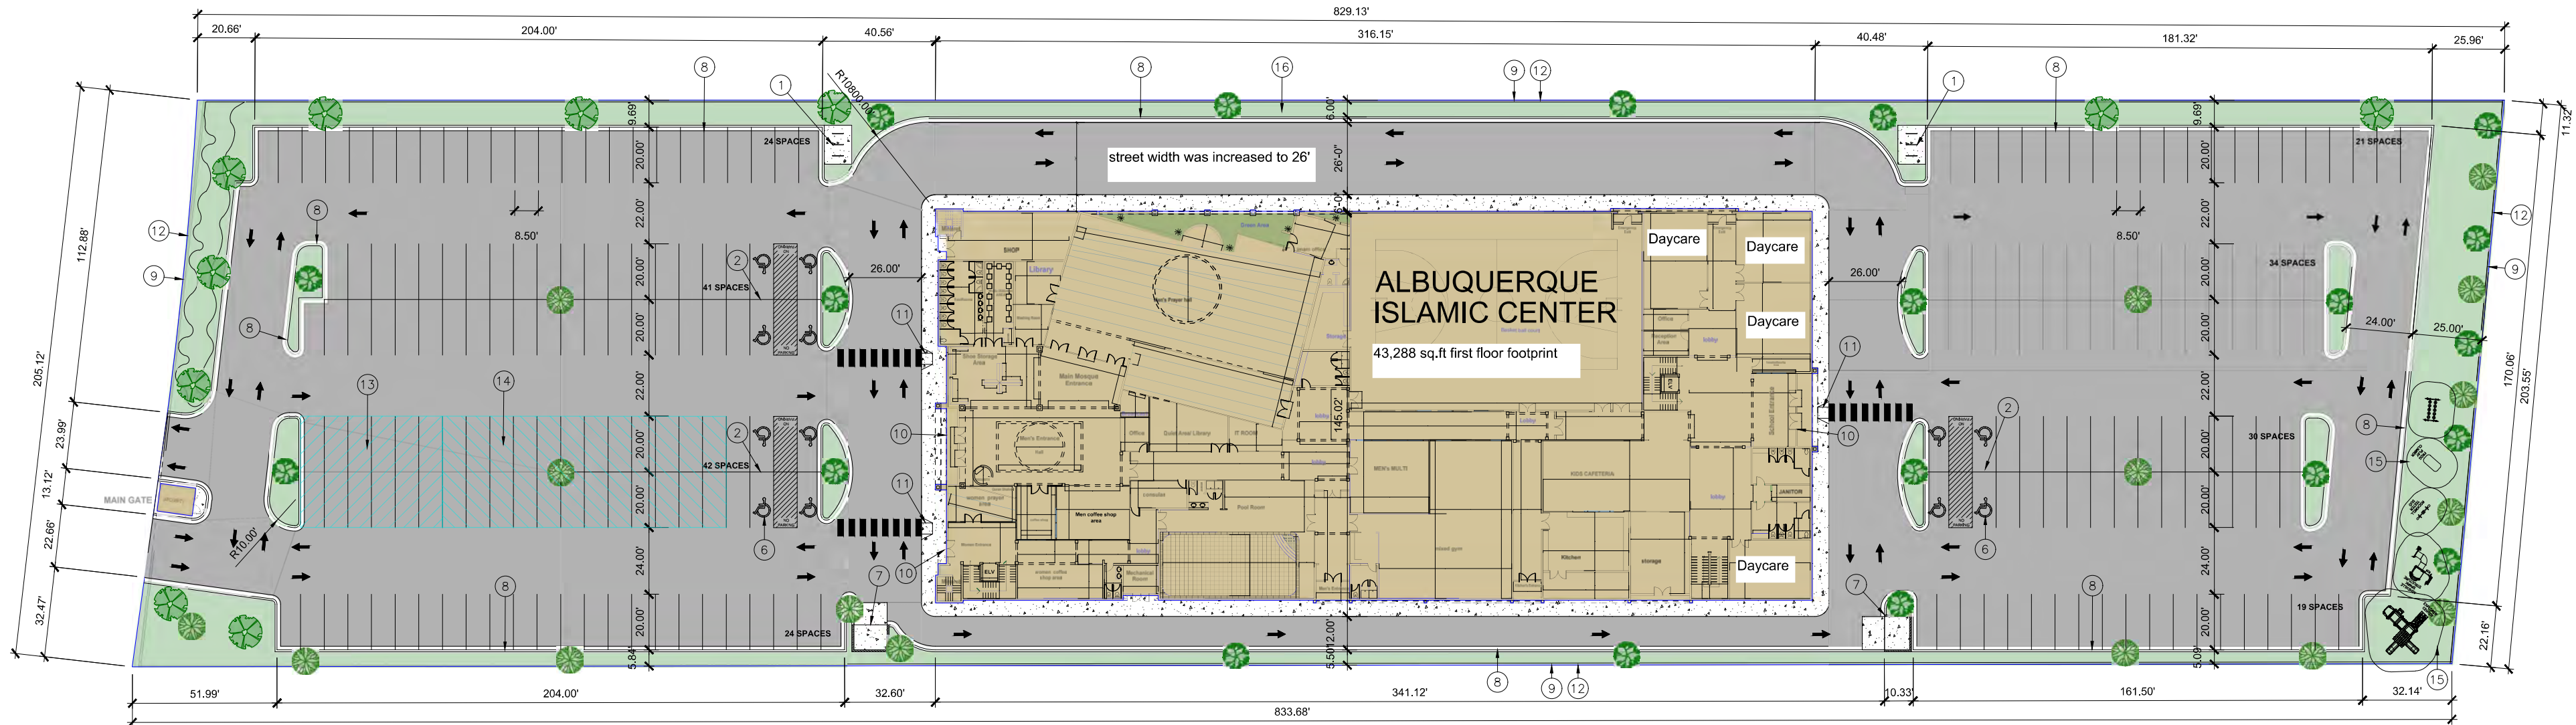

SITE PLAN

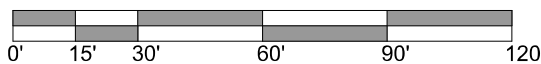

SCALE: 1" = 30'-0"



KEYED NOTES

- 6 SPACE BIKE RACK
- H.C. PARKING SIGN
- NEW FIRE HYDRANT
- NEW 6" SIDEWALK, 2% MAX CROSS SLOPE, 1.5% PREFERRED CROSS SLOPE
- FIRE DEPT. CONNECTION
- H.C. PARKING SYMBOL
- REFUSE ENCLOSURE
- CURB
- EXISTING PROPERTY LINE
- BUILDING ENTRANCE
- CURB RAMP
- 6" CMU WALL
- EVSE SPACES
- EV CAPABLE SPACES
- PLAYGROUND
- MIN. 6' WIDE LANDSCAPE BUFFER



AREA MAP

SCALE: NTS



GENERAL NOTES:

- ALL IMPROVEMENTS LOCATED IN THE RIGHT OF WAY MUST BE INCLUDED IN ON A PUBLIC WORK ORDER.
- LANDSCAPING, FENCING AND SIGNING WILL NOT INTERFERE WITH CLEAR SIGHT REQUIREMENTS. THEREFORE, SIGNS, WALLS, TREES AND SHRUBBERY BETWEEN 3 AND 8 FEET TALL (AS MEASURED FROM THE GUTTER PAN) WILL NOT BE ACCEPTABLE IN THE CLEAR SIGHT TRIANGLE.
- ALL PAVING SHALL BE SHALL BE ASPHALT UNLESS NOTED OTHERWISE, REF. DETAIL THIS SHEET.
- ALL MECHANICAL EQUIPMENT SHALL BE SCREENED IN ACCORDANCE WITH IDO SECTION 5-5 (G).
- ALL OUTDOOR LIGHT FIXTURES SHALL BE LED. FIXTURES 70 WATTS OR GREATER SHALL BE SHIELDED USING FULL CUTOFF LIGHT FIXTURES.
- BUILDING MOUNTED SIGNS SHALL BE EXTERNALLY ILLUMINATED AND SHALL NOT EXTEND MORE THAN 2 FEET ABOVE THE EXTERIOR WALLS OF THE BUILDING.
- WORK WITHIN THE PUBLIC RIGHT OF WAY REQUIRES A WORK ORDER.
- SITE LIGHTING WILL BE PROVIDED BY LIGHT BOLLARDS AND WALL MOUNTED FIXTURES AND SHALL COMPLY WITH 5-8 OF THE IDO
- ROOFTOP SHALL BE BUILT WITH NECESSARY SOLAR INFRASTRUCTURE INCLUDING BUT NOT LIMITED TO ELECTRICAL CONDUIT AND GEAR AND STRUCTURAL SUPPORT
- ALL PARKING LOT PAVING SHALL BE COOL SURFACE TREATMENT
- ALL EXISTING ADA CURB RAMPS SHALL BE UPDATED TO CURRENT STANDARDS AND HAVE TRUNCATED DOMES INSTALLED
- ALL BROKEN OR CRACKED SIDEWALK MUST BE REPLACED WITH SIDEWALK AND CURB & GUTTER.

UPC: 101606428751910308
LEGAL: MAP 24 TRACT 208B
ZONING: A-1
ZONE ATLAS PAGE: B16 / C16
AREA PLAN: NORTH VALLEY AREA PLAN
EXISTING SPECIAL USE PERMIT: ZA2024-0074

GROSS LOT AREA = 3.87 AC = 166,577 SF
BUILDING FOOTPRINT = 43,288 Sq ft
NET LOT AREA = 123,277 SF
LANDSCAPING REQUIRED: 123,277 X 15% = 18,491 SF
LANDSCAPING PROVIDED = 19,726 SF

PARKING:
PLACE OF WORSHIP: 1 SPACE PER 4 SEATS X 615 = 154 SPACES
School: 3 spaces per classroom x 16=48 spaces
Space required = 154 spaces*
Space provided= 235 spaces please see the written statement

ADA PARKING:
PER NMBC TABLE 1106
101-300: 8 SPACES REQUIRED
12 PROVIDED ALL VAN ACCESSIBLE

BICYCLE
1 BICYCLE SPACE PER 20 VEHICLE SPACES = 12 SPACES
12 SPACES PROVIDED

LEGEND

- BUILDING
- CONCRETE
- ASPHALT PAVING
- LANDSCAPE
- CLEAR SIGHT TRIANGLE

No	Revision Item	Date

ALBUQUERQUE ISLAMIC CENTER
9600 2nd ST NW
ALBUQUERQUE, NM 87114


DRAWING TITLE

SITE PLAN

DESIGNED	PROJECT NO
DRAWN	SCALE
CHECKED	DRAWING NO
REVIEWED	
DATE	4/6/2026




S -100

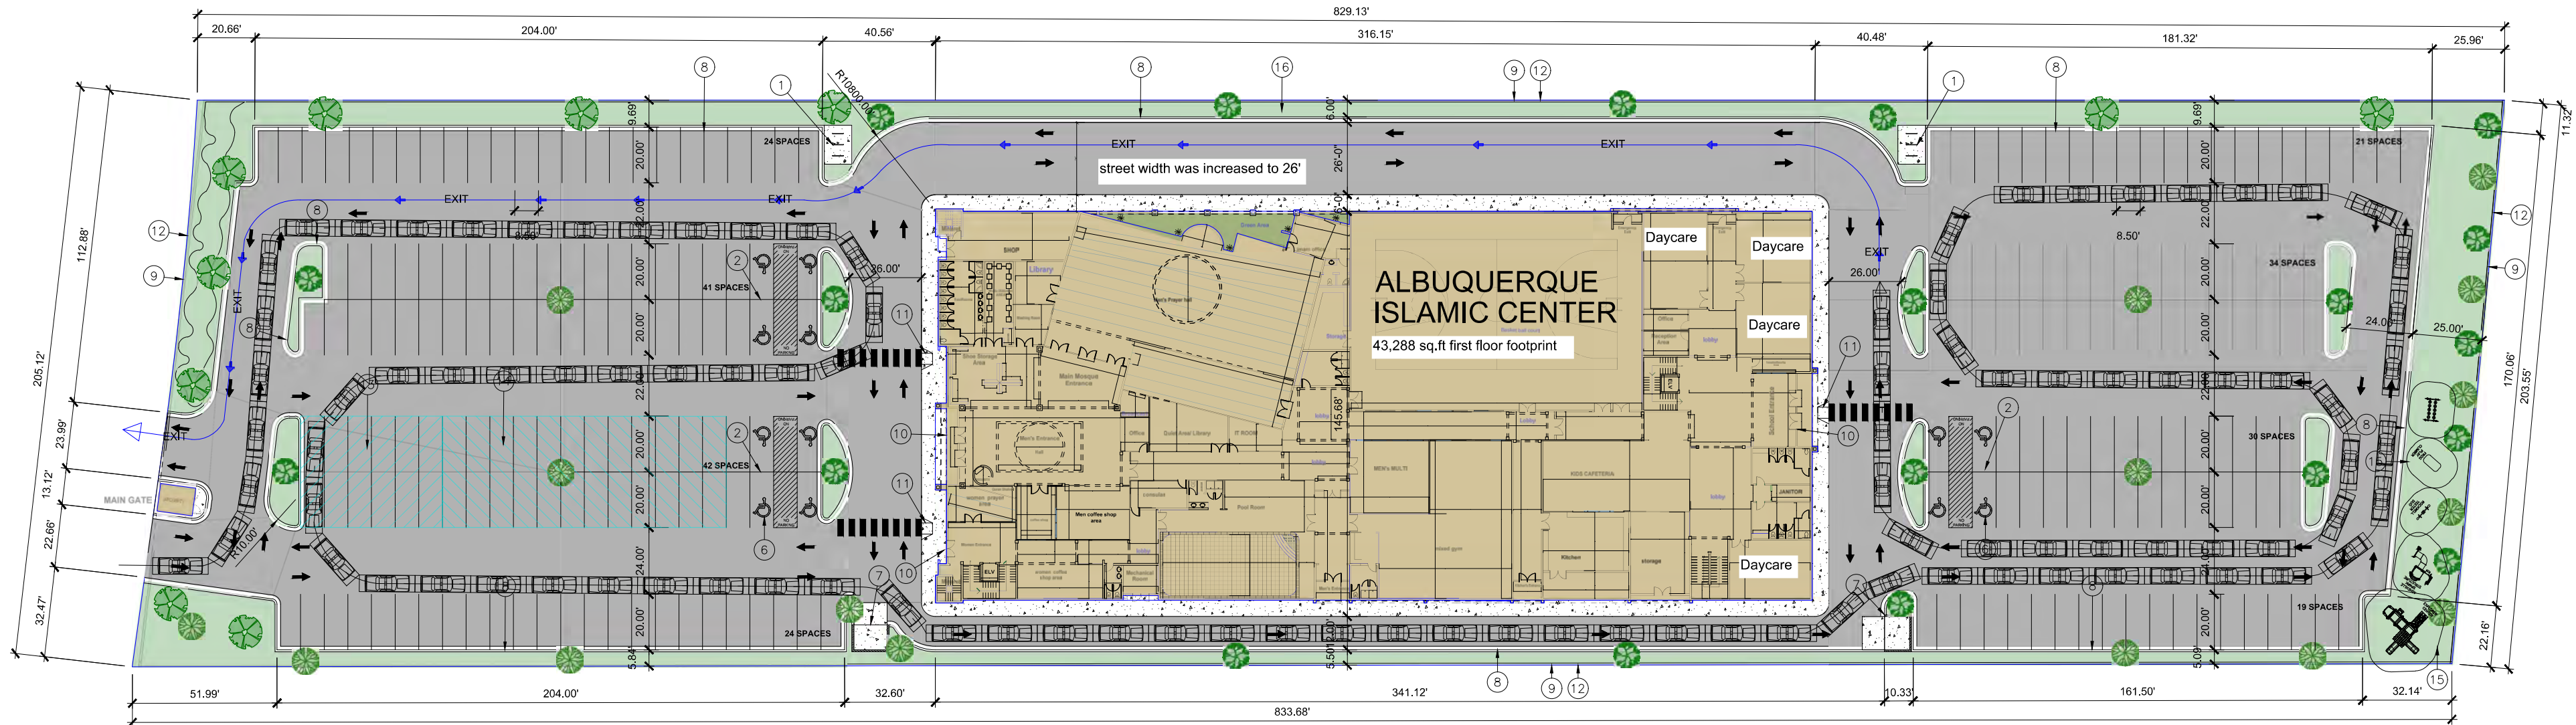

Conceptual School dropoff traffic control plan

SCALE: 1" = 30'-0"

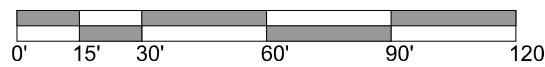


Important Traffic Notice:
The drop-off line can hold up to 110 cars.
Please note that parking on Main Street is strictly prohibited during pick-up and drop-off times.



KEYED NOTES

- 6 SPACE BIKE RACK
- H.C. PARKING SIGN
- NEW FIRE HYDRANT
- NEW 6" SIDEWALK, 2% MAX CROSS SLOPE, 1.5% PREFERRED CROSS SLOPE
- FIRE DEPT. CONNECTION
- H.C. PARKING SYMBOL
- REFUSE ENCLOSURE
- CURB
- EXISTING PROPERTY LINE
- BUILDING ENTRANCE
- CURB RAMP
- 6" CMU WALL
- EVSE SPACES
- EV CAPABLE SPACES
- PLAYGROUND
- MIN. 6' WIDE LANDSCAPE BUFFER

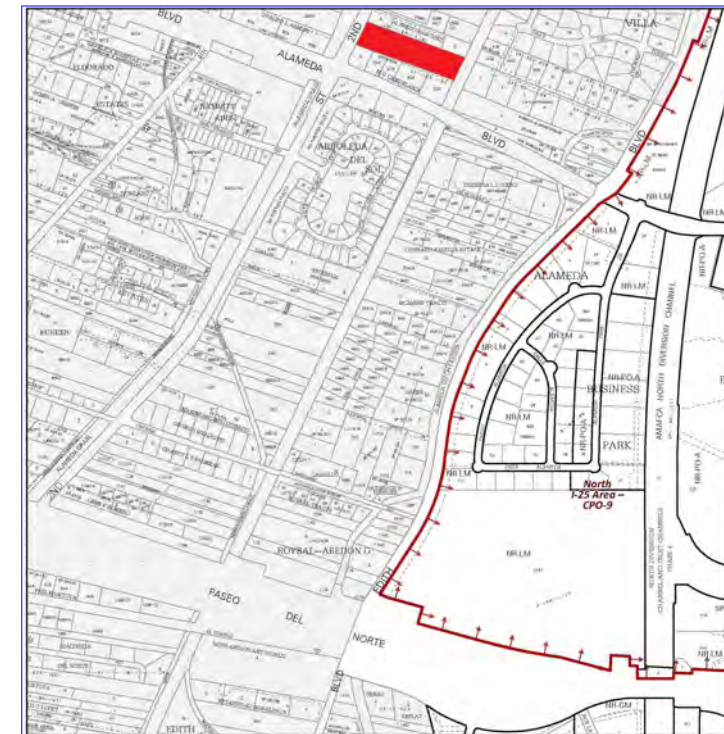

AREA MAP

SCALE: NTS



GENERAL NOTES:

ALL IMPROVEMENTS LOCATED IN THE RIGHT OF WAY MUST BE INCLUDED IN ON A PUBLIC WORK ORDER.

LANDSCAPING, FENCING AND SIGNING WILL NOT INTERFERE WITH CLEAR SIGHT REQUIREMENTS. THEREFORE, SIGNS, WALLS, TREES AND SHRUBBERY BETWEEN 3 AND 8 FEET TALL (AS MEASURED FROM THE GUTTER PAN) WILL NOT BE ACCEPTABLE IN THE CLEAR SIGHT TRIANGLE.

ALL PAVING SHALL BE SHALL BE ASPHALT UNLESS NOTED OTHERWISE, REF. DETAIL THIS SHEET.

ALL MECHANICAL EQUIPMENT SHALL BE SCREENED IN ACCORDANCE WITH IDO SECTION 5-5 (G).

ALL OUTDOOR LIGHT FIXTURES SHALL BE LED. FIXTURES 70 WATTS OR GREATER SHALL BE SHIELDED USING FULL CUTOFF LIGHT FIXTURES.

BUILDING MOUNTED SIGNS SHALL BE EXTERNALLY ILLUMINATED AND SHALL NOT EXTEND MORE THAN 2 FEET ABOVE THE EXTERIOR WALLS OF THE BUILDING.

WORK WITHIN THE PUBLIC RIGHT OF WAY REQUIRES A WORK ORDER.

SITE LIGHTING WILL BE PROVIDED BY LIGHT BOLLARDS AND WALL MOUNTED FIXTURES AND NOT LIMITED TO ELECTRICAL CONDUIT AND GEAR AND STRUCTURAL SUPPORT

ROOFTOP SHALL BE BUILT WITH NECESSARY SOLAR INFRASTRUCTURE INCLUDING BUT NOT LIMITED TO ELECTRICAL CONDUIT AND GEAR AND STRUCTURAL SUPPORT

ALL PARKING LOT PAVING SHALL BE COOL SURFACE TREATMENT

ALL EXISTING ADA CURB RAMPS SHALL BE UPDATED TO CURRENT STANDARDS AND HAVE TRUNCATED DOMES INSTALLED

ALL BROKEN OR CRACKED SIDEWALK MUST BE REPLACED WITH SIDEWALK AND CURB & GUTTER.

UPC: 101606428751910308
LEGAL: MAP 24 TRACT 2088
ZONING: A-1
ZONE ATLAS PAGE: B16 / C16
AREA PLAN: NORTH VALLEY AREA PLAN
EXISTING SPECIAL USE PERMIT: ZA2024-0074

GROSS LOT AREA = 3.87 AC = 168,577 SF
BUILDING FOOTPRINT = 43,288 Sq ft
NET LOT AREA = 123,277 SF
LANDSCAPING REQUIRED: 123,277 X 15% = 18,491 SF
LANDSCAPING PROVIDED = 19,726 SF

ADA PARKING:
PER NMBC TABLE 1106
101-300: 8 SPACES REQUIRED
12 PROVIDED ALL VAN ACCESSIBLE

BICYCLE
1 BICYCLE SPACE PER 20 VEHICLE SPACES = 12 SPACES
12 SPACES PROVIDED

LEGEND

- BUILDING
- CONCRETE
- ASPHALT PAVING
- LANDSCAPE
- CLEAR SIGHT TRIANGLE


No	Revision Item	Date




ALBUQUERQUE ISLAMIC CENTER
9600 2nd ST NW
ALBUQUERQUE, NM 87114


DRAWING TITLE
SITE PLAN

DESIGNED	PROJECT NO
DRAWN	SCALE
CHECKED	DRAWING NO
REVIEWED	
DATE	4/6/2026

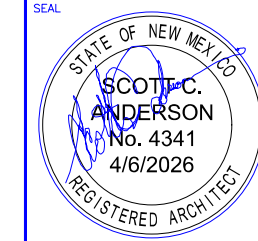


C-100

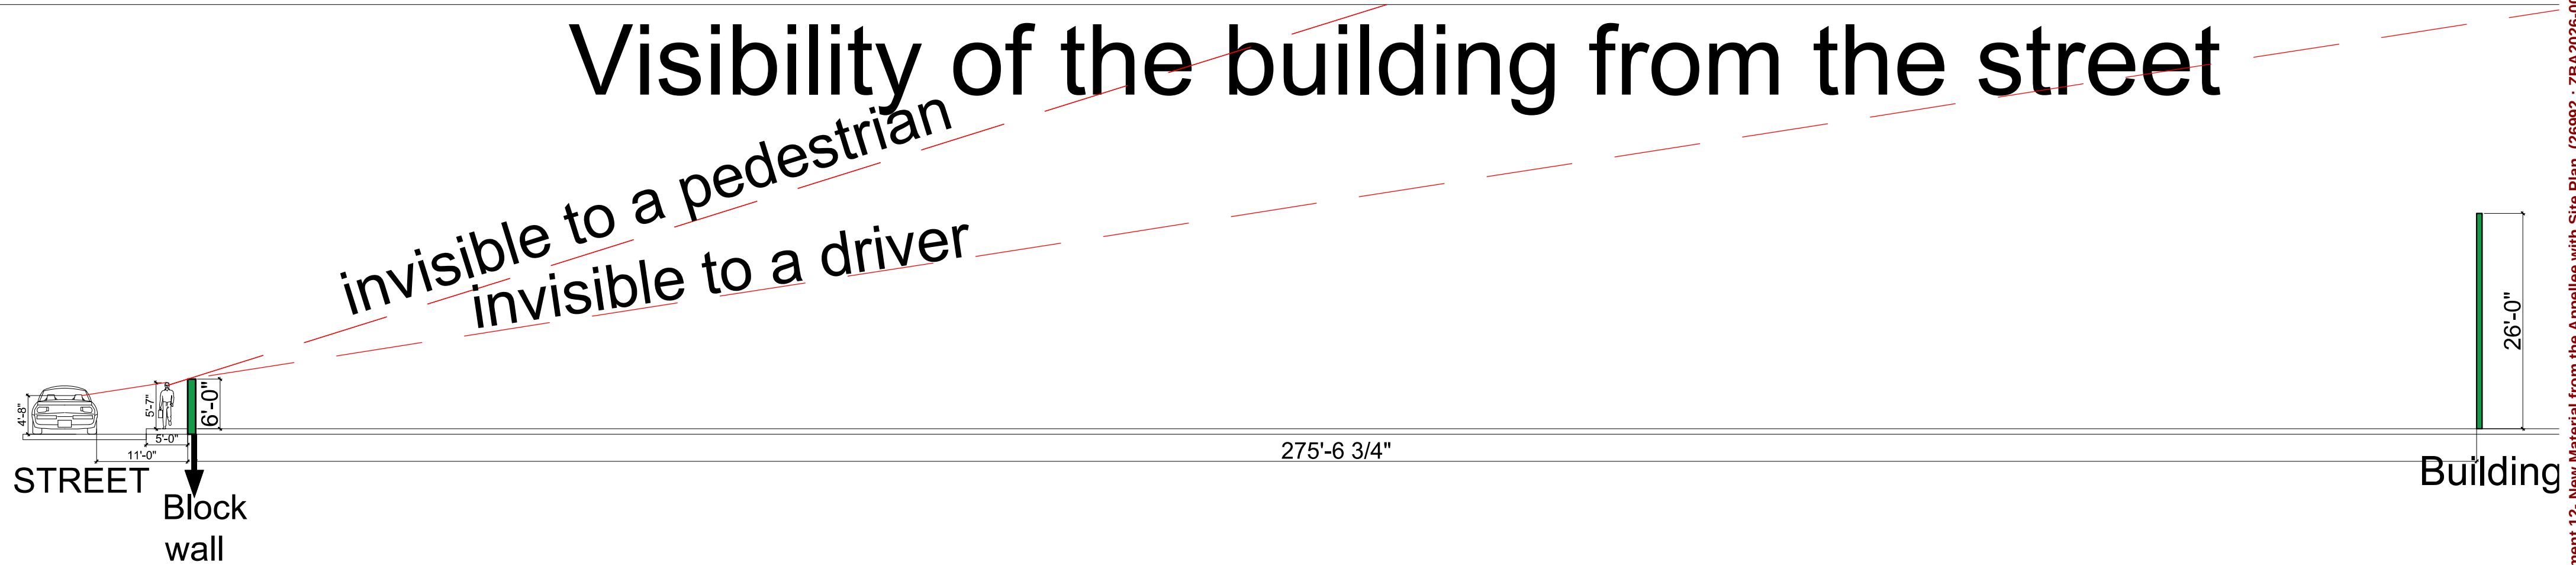

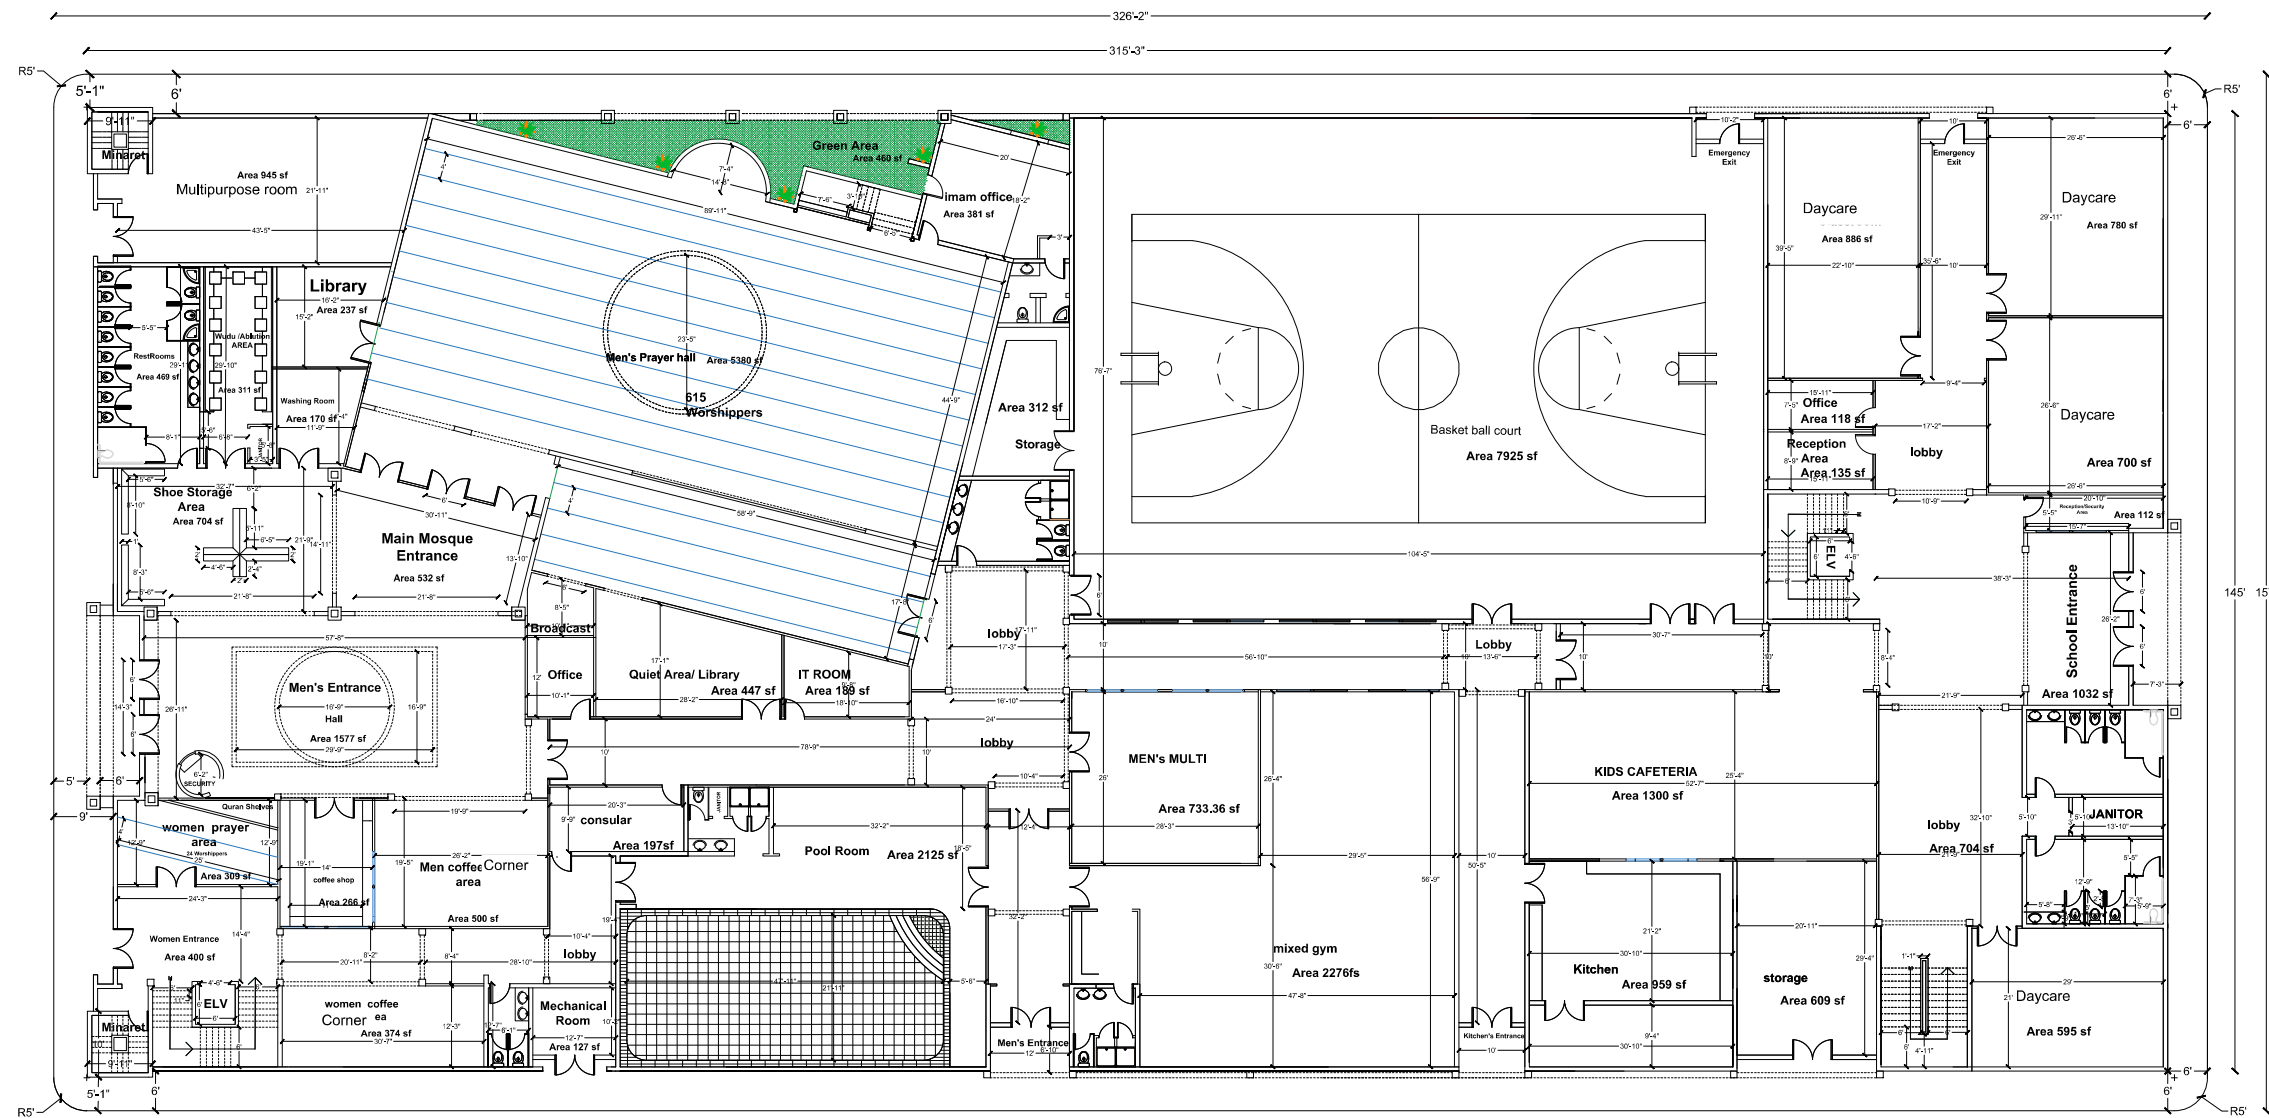

FRIST FLOOR

SCALE: 1/20" = 1'-0"

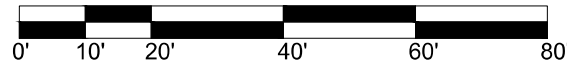

No	Revision Item	Date
ISLAMIC CENTER PLAN		
DRAWING TITLE FRIST FLOOR		
SEAL	DESIGNED	PROJECT NO
	DRAWN	SCALE
	CHECKED	DRAWING NO
	REVIEWED	A-200 _____ OF _____
	DATE 9/11/2025	